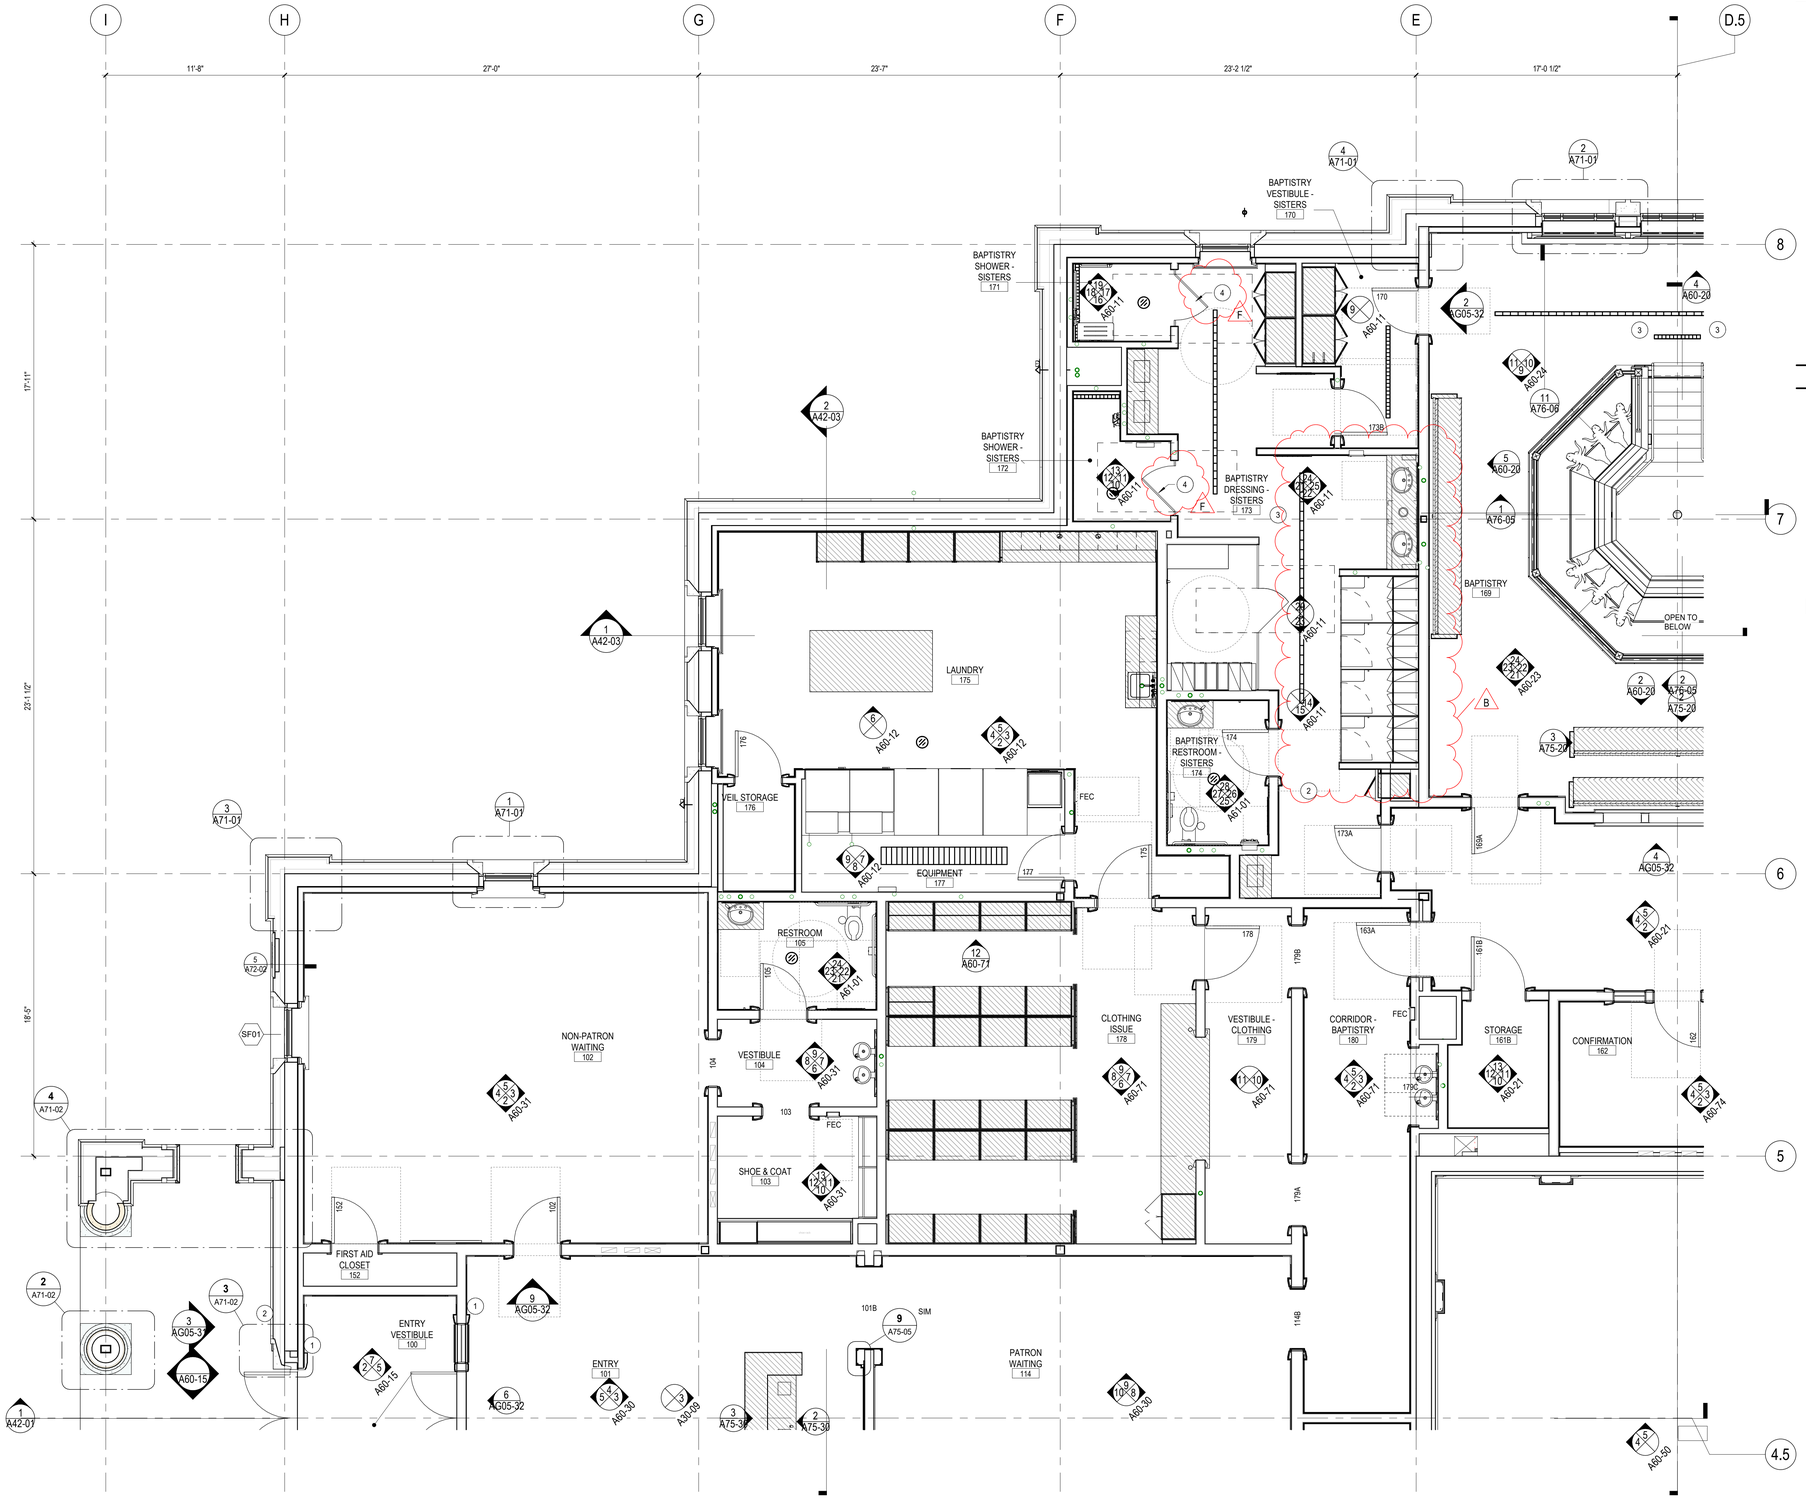

1 A20-05 FLOOR PLAN - LEVEL 01 AREA A

SCALE: 1/4" = 1'-0"

GENERAL NOTES - FLOOR PLAN

1. READ IN CONJUNCTION WITH PROJECT SPECIFICATIONS.
2. ADVISE CONSULTANT OF DISCREPANCIES WITH THE DIMENSION PLANS OR CONFLICTS WITH OTHER PARTS OF THE WORK. ADJUST LOCATIONS AS REQUIRED BASED ON REVIEW.
3. ALL GYPSUM BOARD PARTITIONS SHALL BE LEVEL 5 FINISH; TAPED, SPACKLED AND SANDED WITH NO VISIBLE JOINTS. ALL SURFACES SHALL BE ALIGNED.
4. WHERE FURRED PARTITIONS EXCEED MAXIMUM HEIGHT, BRACE TO ADJACENT STRUCTURE.
5. FIRE SAFE PENETRATIONS AT RATED PARTITIONS PER APPLICABLE ULC ASSEMBLY.
6. ALL INTERIOR PARTITIONS, PENETRATIONS AND OTHER OPENINGS IN THE BUILDING SHALL BE SEALED, GASKETED OR WEATHER STRIPPED.
7. PROVIDE FIRE TREATED BLOCKING AS REQUIRED AT LOCATIONS INCLUDING BUT NOT LIMITED TO GRAB BARS, SHELVING, OVERHEAD CABINETS, TOILET ROOMS, ACCESSORIES, EQUIPMENT, ETC.
8. ALL DIMENSIONS ARE FROM THE FACE OF STUD, UNLESS OTHERWISE NOTED.
9. ALL WOOD TO BE FIRE RETARDANT TREATED IN ACCORDANCE WITH LOCAL CODES.
10. ALL DIMENSIONS MARKED "CLEAR" OR "CLR" SHALL BE MAINTAINED AND SHALL ALLOW FOR THICKNESS OF ALL WALL FINISHES. THESE DIMENSIONS SHALL NOT VARY MORE THAN +/- 1/8" WITHOUT WRITTEN CONSENT FROM THE ARCHITECT.
11. ALL CASEWORK TO BE PREMIUM GRADE OR BETTER AS DEFINED BY THE ARCHITECTURAL WOOD INSTITUTE.
12. EDGES OF ALL DOOR CASINGS TO BE 4" FROM CORNER OF ROOM UNLESS NOTED OTHERWISE.
13. FOR WALL TYPES, SEE AG04 SERIES SHEETS.

FLOOR PLAN GRAPHIC LEGEND

SEE A01-20 FOR ALL GENERAL NOTES, ABBREVIATIONS, AND SYMBOLS

ROOM TAG
ROOM NAME — ROOM NAME
000 — ROOM NUMBER

WALL TAG
P1A — WALL TYPE
VARIANT (IF APPLICABLE)

DOOR TAG
000 — DOOR NUMBER

SECTION TAG
SIM — SIMILAR (IF APPLICABLE)
1 A00-00 — VIEW NUMBER
SHEET NUMBER

EXTERIOR ELEVATION TAG
SIM — SIMILAR (IF APPLICABLE)
1 A00-00 — VIEW NUMBER
SHEET NUMBER

INTERIOR ELEVATION TAG
1 A60-00 — VIEW NUMBER (TYP.)
SHEET NUMBER

CALLOUT TAGS
SIM — SIMILAR (IF APPLICABLE)
1 A00-00 — VIEW NUMBER
SHEET NUMBER

MATCHLINE TAGS
VIEW NUMBER (ABOVE MATCHLINE)
MATCHLINE, SEE: 1/A00-00 — SHEET NUMBER (ABOVE MATCHLINE)
MATCHLINE, SEE: 1/A00-00 — SHEET NUMBER (BELOW MATCHLINE)
VIEW NUMBER (BELOW MATCHLINE)

CLEARANCES
ø 5'-0" — WHEELCHAIR CLEARANCE
2'-6" / 4'-0" — SINK & URINAL CLEARANCE
5'-0" / 4'-8" — TOILET CLEARANCE
1'-6" / 5'-0" / 1'-0" / 4'-0" — DOOR CLEARANCE

EXTERIOR WALL SECTION TAG
SIM — SIMILAR (IF APPLICABLE)
1 A00-00 — VIEW NUMBER
SHEET NUMBER

FIRE RATINGS
1HR FRR
2HR FRR

HATCH PATTERNS
MILLWORK

SHEET NOTE SCHEDULE

#	DESCRIPTION
1	TOUCHLESS ACTUATOR CONTROL FOR DOOR AUTO OPERATOR. BASIS OF DESIGN: LCN 8310-810S. REFER TO INTERIOR ELEVATIONS.
2	KNOXBOX - FINAL LOCATION TBD. TO BE TIED INTO SECURITY SYSTEM.
3	LINEAR FLOOR DRAIN. SEE PLUMBING DRAWINGS FOR MORE INFO.
4	PHENOLIC SHOWER DOOR

DATE	ISSUED FOR	REV
01/11/2024	ISSUE FOR 100%CD	A
21/03/2025	ADDENDUM 1 - OWNER REQUESTED PLAN REVISIONS	B
21/03/2025	ADDENDUM 1 - ONGOING COORDINATION	F

North Arrow

TRUE NORTH

This drawing has been prepared solely for the use of THE CHURCH OF JESUS CHRIST OF LATTER -DAY SAINTS and there are no representations of any kind made by NORR to any party with whom NORR has not entered into a contract.

This drawing shall not be used for construction purposes until the seal appearing hereon is signed and dated by the Architect or Engineer

Project Component
CONSTRUCTION DOCUMENTS

Key Plan

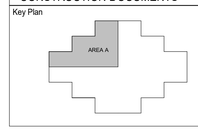

Consultants

Survey: SIEGFRIED, 3428 BROOKSIDE ROAD, STOCKON, CA 95219
Civil: SIEGFRIED, 3428 BROOKSIDE ROAD, STOCKON, CA 95219
Architectural: NORR, 2020 I STREET, SUITE 200, SACRAMENTO, CA 95816
Structural: BUEHLER, 600 Q STREET #200, SACRAMENTO, CA 95811
Mechanical: GLUMAC, 150 S 4TH STREET UNIT A, HENDERSION, NV 89015
Electrical: GLUMAC, 150 S 4TH STREET UNIT A, HENDERSION, NV 89015
Interiors: SAGRADA, 565 N. DE SOTO ST E, SALT LAKE CITY, UT 84103
Landscape: SIEGFRIED, 3428 BROOKSIDE ROAD, STOCKTON, CA 95219

Seal(s)

NORR
2020 I Street, Suite 200
Sacramento, CA 95816, United States
916.930.0210
norr.com

Project Manager: ANDREA JAGGERS	Drawn: Author
Project Leader: JULIAN ANDRADE	Checked: Checker

Client
THE CHURCH OF JESUS CHRIST OF LATTER-DAY SAINTS

Project
NEW TEMPLE PROJECT

771 W. Fremont Ave. Sunnyvale, CA 94087

Drawing Title
ENLARGED FLOOR PLAN - LEVEL 01 - AREA A

Scale: 1/4" = 1'-0"

Project No.: ED2024-0005-00

Drawing No.: **A20-05**

ARCH E Title Block - v.2024 - Rev (June/24) - Copyright © 2024

3/19/2025 11:37:39 AM
Autodesk Docs://LDS_Temple_San Jose, CA/NORR_ED2024-0005_AR_SanJoseTemple_Interior_R24.rvt

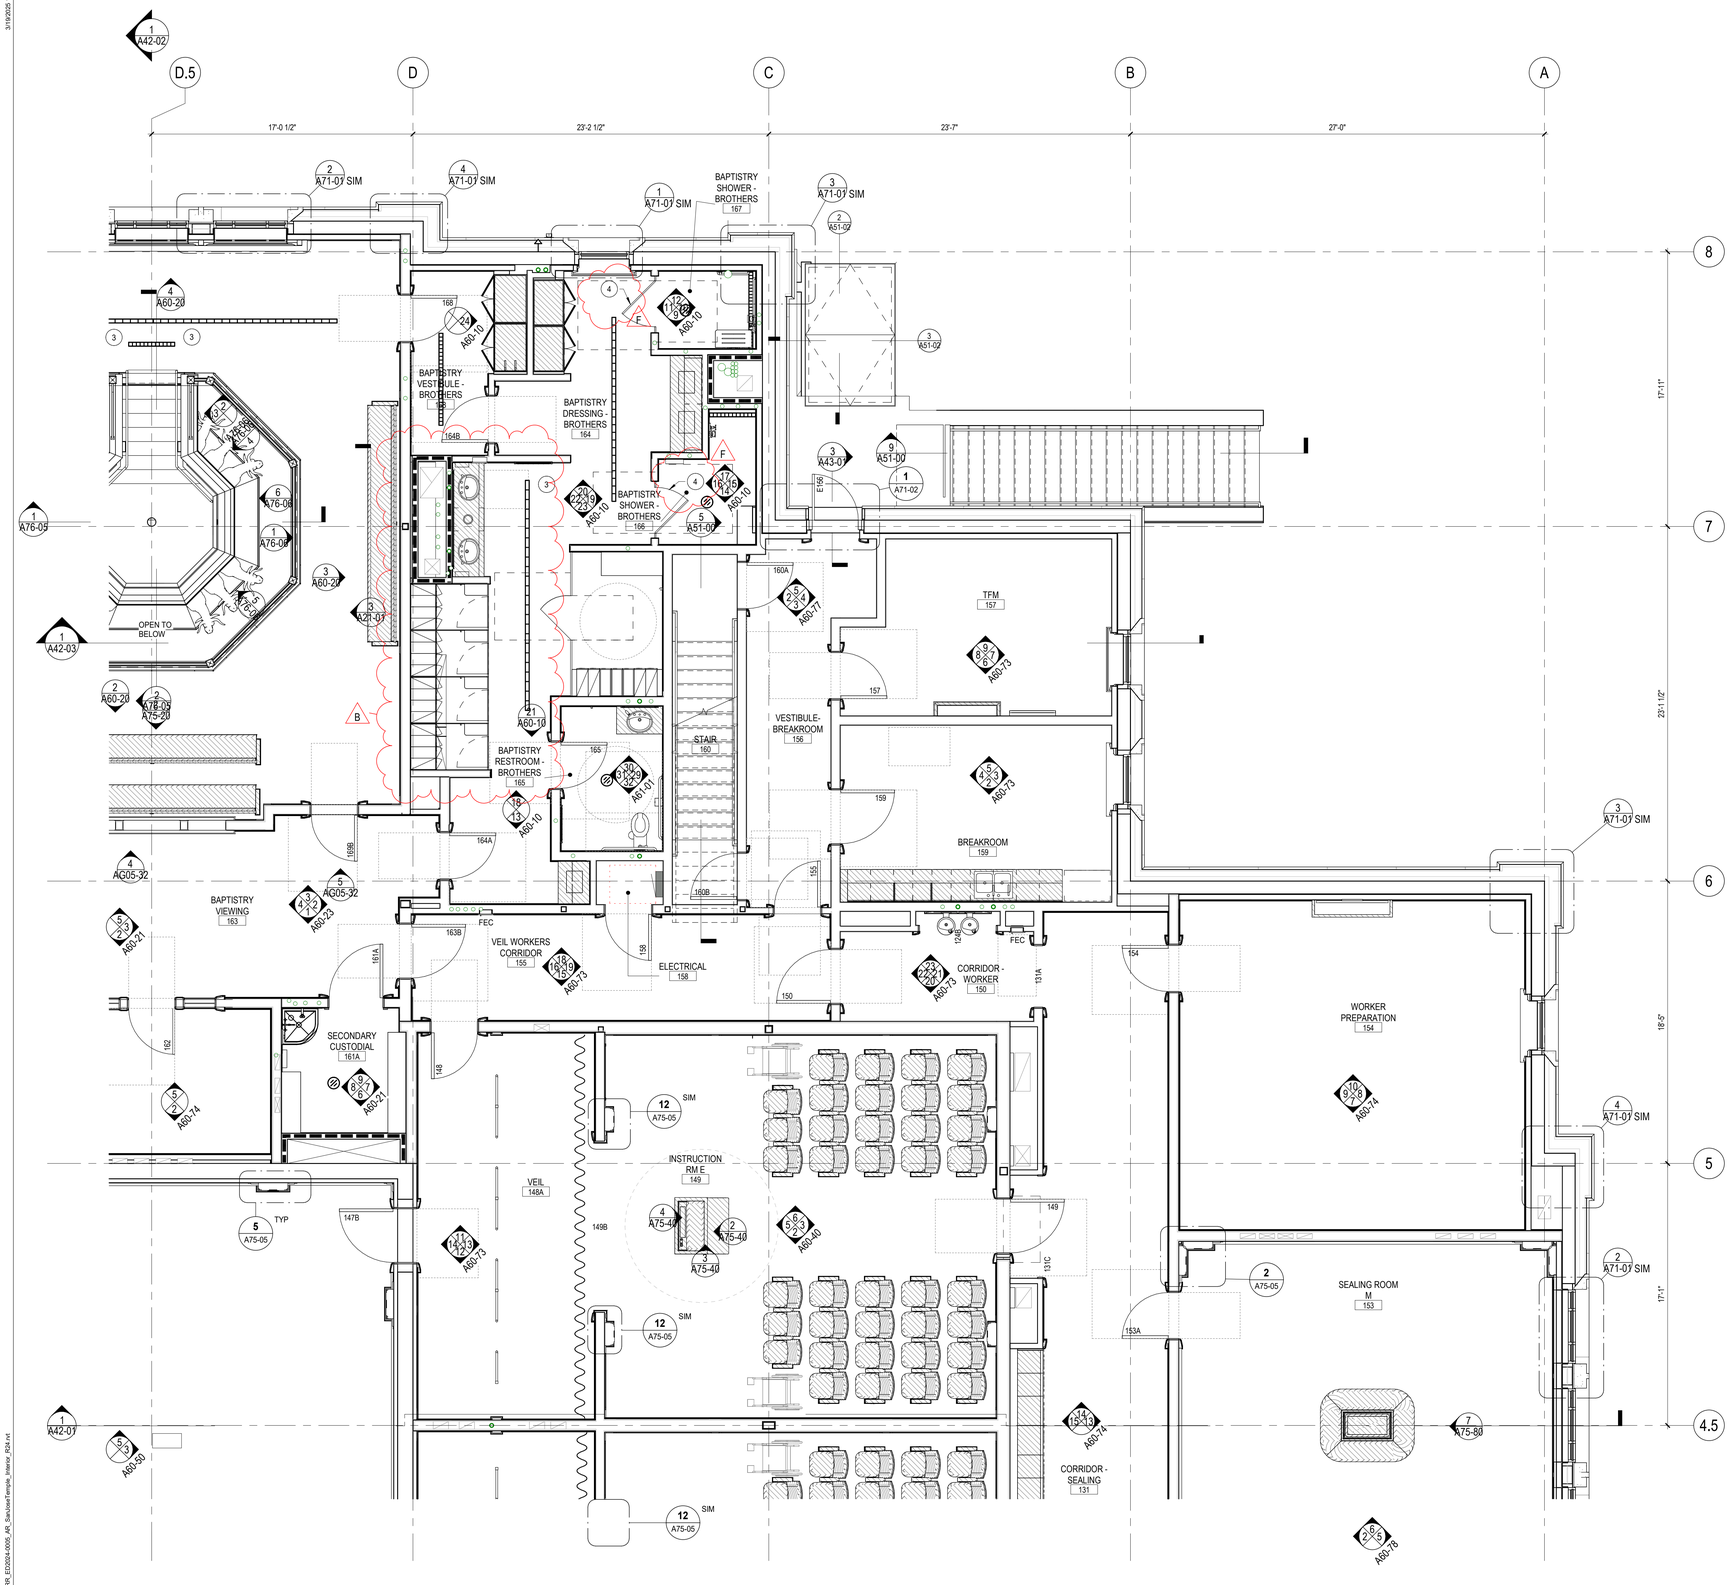

1 A20-06 FLOOR PLAN - LEVEL 01 AREA B

SCALE: 1/4" = 1'-0"

GENERAL NOTES - FLOOR PLAN

1. READ IN CONJUNCTION WITH PROJECT SPECIFICATIONS.
2. ADVISE CONSULTANT OF DISCREPANCIES WITH THE DIMENSION PLANS OR CONFLICTS WITH OTHER PARTS OF THE WORK. ADJUST LOCATIONS AS REQUIRED BASED ON REVIEW.
3. ALL GYPSUM BOARD PARTITIONS SHALL BE LEVEL 5 FINISH; TAPED, SPACKLED AND SANDED WITH NO VISIBLE JOINTS. ALL SURFACES SHALL BE ALIGNED.
4. WHERE FURRED PARTITIONS EXCEED MAXIMUM HEIGHT, BRACE TO ADJACENT STRUCTURE.
5. FIRE SAFE PENETRATIONS AT RATED PARTITIONS PER APPLICABLE ULC ASSEMBLY.
6. ALL INTERIOR PARTITIONS, PENETRATIONS AND OTHER OPENINGS IN THE BUILDING SHALL BE SEALED, GASKETED OR WEATHER STRIPPED.
7. PROVIDE FIRE TREATED BLOCKING AS REQUIRED AT LOCATIONS INCLUDING BUT NOT LIMITED TO GRAB BARS, SHELVING, OVERHEAD CABINETS, TOILET ROOMS, ACCESSORIES, EQUIPMENT, ETC.
8. ALL DIMENSIONS ARE FROM THE FACE OF STUD, UNLESS OTHERWISE NOTED.
9. ALL WOOD TO BE FIRE RETARDANT TREATED IN ACCORDANCE WITH LOCAL CODES.
10. ALL DIMENSIONS MARKED "CLEAR" OR "CLR" SHALL BE MAINTAINED AND SHALL ALLOW FOR THICKNESS OF ALL WALL FINISHES. THESE DIMENSIONS SHALL NOT VARY MORE THAN +/- 1/8" WITHOUT WRITTEN CONSENT FROM THE ARCHITECT.
11. ALL CASEWORK TO BE PREMIUM GRADE OR BETTER AS DEFINED BY THE ARCHITECTURAL WOOD INSTITUTE.
12. EDGES OF ALL DOOR CASINGS TO BE 4" FROM CORNER OF ROOM UNLESS NOTED OTHERWISE.
13. FOR WALL TYPES, SEE AG04 SERIES SHEETS.

FLOOR PLAN GRAPHIC LEGEND

SEE A01-20 FOR ALL GENERAL NOTES, ABBREVIATIONS, AND SYMBOLS

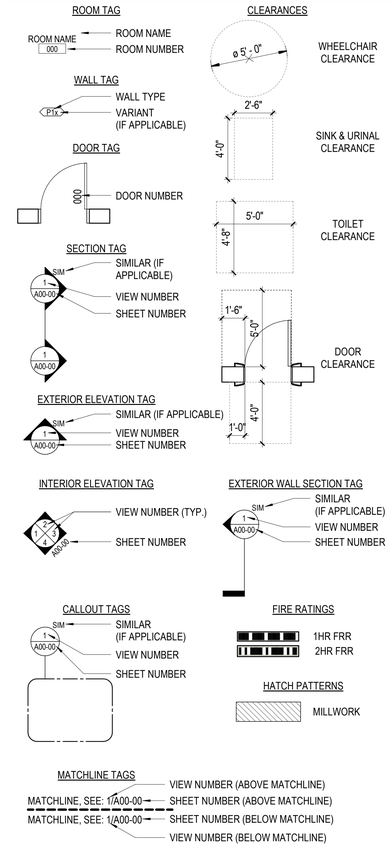

SHEET NOTE SCHEDULE

#	DESCRIPTION
3	LINEAR FLOOR DRAIN. SEE PLUMBING DRAWINGS FOR MORE INFO.
4	PHENOLIC SHOWER DOOR

DATE	ISSUED FOR	REV
01/11/2024	ISSUE FOR 100%CD	A
21/03/2025	ADDENDUM 1 - OWNER REQUESTED PLAN REVISIONS	B
21/03/2025	ADDENDUM 1 - ONGOING COORDINATION	F

North Arrow

TRUE NORTH

This drawing has been prepared solely for the use of THE CHURCH OF JESUS CHRIST OF LATTER -DAY SAINTS and there are no representations of any kind made by NORR to any party with whom NORR has not entered into a contract.

This drawing shall not be used for construction purposes until the seal appearing hereon is signed and dated by the Architect or Engineer

Project Component

CONSTRUCTION DOCUMENTS

Key Plan

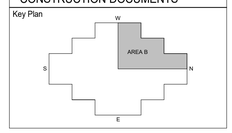

Consultants

Survey: SIEGFRIED, 3428 BROOKSIDE ROAD, STOCKON, CA 95219
Civil: SIEGFRIED, 3428 BROOKSIDE ROAD, STOCKON, CA 95219
Architectural: NORR, 2020 I STREET, SUITE 200, SACRAMENTO, CA 95816
Structural: BUEHLER, 600 Q STREET #200, SACRAMENTO, CA 95811
Mechanical: GLUMAC, 150 S 4TH STREET UNIT A, HENDERSON, NV 89015
Electrical: GLUMAC, 150 S 4TH STREET UNIT A, HENDERSON, NV 89015
Interiors: SAGRADA, 565 N. DE SOTO ST E, SALT LAKE CITY, UT 84103
Landscape: SIEGFRIED, 3428 BROOKSIDE ROAD, STOCKTON, CA 95219

Seal(s)

NORR
2020 I Street, Suite 200
Sacramento, CA 95816, United States
916.930.0210
norr.com

Project Manager	Drawn
ANDREA JAGGERS	Author
Project Leader	Checked
JULIAN ANDRADE	Checker

Client

THE CHURCH OF JESUS CHRIST OF LATTER-DAY SAINTS

Project

NEW TEMPLE PROJECT

771 W. Fremont Ave, Sunnyvale, CA 94087

Drawing Title

ENLARGED FLOOR PLAN - LEVEL 01 - AREA B

Scale: 1/4" = 1'-0"

Project No.: ED2024-0005-00

Drawing No.: **A20-06**

ARCH E Title Block - v.2024 - Rev (June24) - Copyright © 2024

3/19/2025 11:37:45 AM
Autodesk Docs://JDS_Temple_San Jose_CA/NORR_ED2024-0005_AR_SanJoseTemple_Interior_R24.rvt

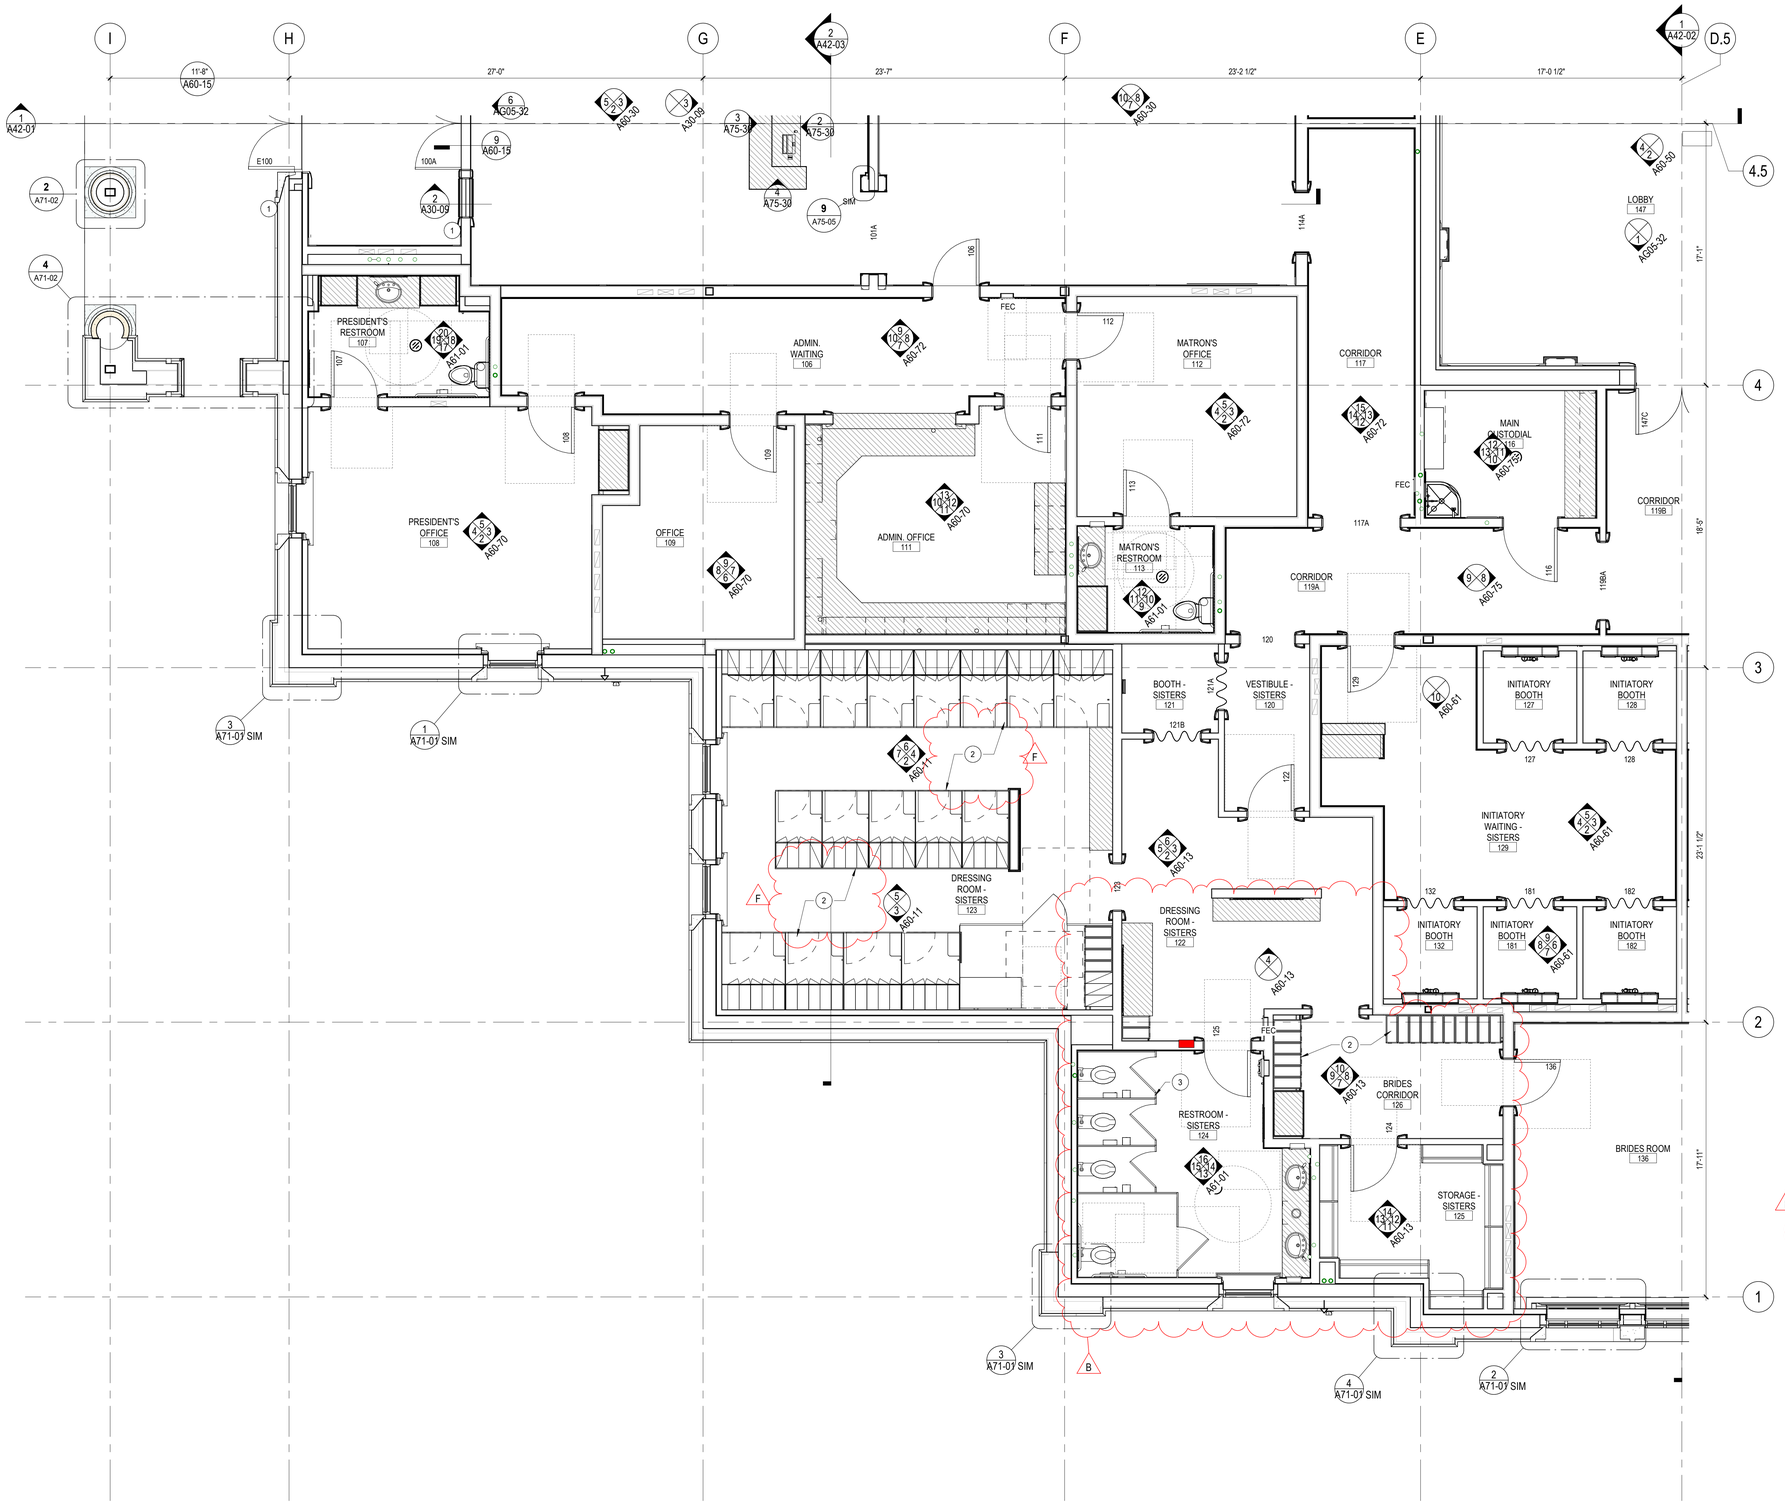

1 A20-07 FLOOR PLAN - LEVEL 01 AREA C

SCALE: 1/4" = 1'-0"

GENERAL NOTES - FLOOR PLAN

1. READ IN CONJUNCTION WITH PROJECT SPECIFICATIONS.
2. ADVISE CONSULTANT OF DISCREPANCIES WITH THE DIMENSION PLANS OR CONFLICTS WITH OTHER PARTS OF THE WORK. ADJUST LOCATIONS AS REQUIRED BASED ON REVIEW.
3. ALL GYPSUM BOARD PARTITIONS SHALL BE LEVEL 5 FINISH; TAPED, SPACKLED AND SANDED WITH NO VISIBLE JOINTS. ALL SURFACES SHALL BE ALIGNED.
4. WHERE FURRED PARTITIONS EXCEED MAXIMUM HEIGHT, BRACE TO ADJACENT STRUCTURE.
5. FIRE SAFE PENETRATIONS AT RATED PARTITIONS PER APPLICABLE ULC ASSEMBLY.
6. ALL INTERIOR PARTITIONS, PENETRATIONS AND OTHER OPENINGS IN THE BUILDING SHALL BE SEALED, GASKETED OR WEATHER STRIPPED.
7. PROVIDE FIRE TREATED BLOCKING AS REQUIRED AT LOCATIONS INCLUDING BUT NOT LIMITED TO GRAB BARS, SHELVING, OVERHEAD CABINETS, TOILET ROOMS, ACCESSORIES, EQUIPMENT, ETC.
8. ALL DIMENSIONS ARE FROM THE FACE OF STUD, UNLESS OTHERWISE NOTED.
9. ALL WOOD TO BE FIRE RETARDANT TREATED IN ACCORDANCE WITH LOCAL CODES.
10. ALL DIMENSIONS MARKED "CLEAR" OR "CLR" SHALL BE MAINTAINED AND SHALL ALLOW FOR THICKNESS OF ALL WALL FINISHES. THESE DIMENSIONS SHALL NOT VARY MORE THAN +/- 1/8" WITHOUT WRITTEN CONSENT FROM THE ARCHITECT.
11. ALL CASEWORK TO BE PREMIUM GRADE OR BETTER AS DEFINED BY THE ARCHITECTURAL WOOD INSTITUTE.
12. EDGES OF ALL DOOR CASINGS TO BE 4" FROM CORNER OF ROOM UNLESS NOTED OTHERWISE.
13. FOR WALL TYPES, SEE AG04 SERIES SHEETS.

FLOOR PLAN GRAPHIC LEGEND

SEE A01-20 FOR ALL GENERAL NOTES, ABBREVIATIONS, AND SYMBOLS

ROOM TAG
- ROOM NAME
- ROOM NUMBER

WALL TAG
- WALL TYPE
- VARIANT (IF APPLICABLE)

DOOR TAG
- DOOR NUMBER

SECTION TAG
- SIMILAR (IF APPLICABLE)
- VIEW NUMBER
- SHEET NUMBER

EXTERIOR ELEVATION TAG
- SIMILAR (IF APPLICABLE)
- VIEW NUMBER
- SHEET NUMBER

INTERIOR ELEVATION TAG
- VIEW NUMBER (TYP.)
- SHEET NUMBER

CALLOUT TAGS
- SIMILAR (IF APPLICABLE)
- VIEW NUMBER
- SHEET NUMBER

MATCHLINE TAGS
- VIEW NUMBER (ABOVE MATCHLINE)
- MATCHLINE, SEE: 1/A00-00 — SHEET NUMBER (ABOVE MATCHLINE)
- MATCHLINE, SEE: 1/A00-00 — SHEET NUMBER (BELOW MATCHLINE)
- VIEW NUMBER (BELOW MATCHLINE)

CLEARANCES
- WHEELCHAIR CLEARANCE (ø 5' - 0")
- SINK & URINAL CLEARANCE (2'-6" x 4'-0")
- TOILET CLEARANCE (5'-0" x 4'-8")
- DOOR CLEARANCE (1'-6" x 5'-0", 4'-0" x 1'-0")

EXTERIOR WALL SECTION TAG
- SIMILAR (IF APPLICABLE)
- VIEW NUMBER
- SHEET NUMBER

FIRE RATINGS
- 1HR FRR
- 2HR FRR

HATCH PATTERNS
- MILLWORK

SHEET NOTE SCHEDULE

#	DESCRIPTION
1	TOUCHLESS ACTUATOR CONTROL FOR DOOR AUTO OPERATOR. BASIS OF DESIGN: LCN 8310-810S, REFER TO INTERIOR ELEVATIONS.
2	PHENOLIC LOCKERS AND DRESSING COMPARTMENTS; COLUMBIA #LDB-3660, TYP.
3	PHENOLIC TOILET PARTITIONS, TYP.

DATE	ISSUED FOR	REV
01/11/2024	ISSUE FOR 100%CD	A
21/03/2025	ADDENDUM 1 - OWNER REQUESTED PLAN REVISIONS	B
21/03/2025	ADDENDUM 1 - ONGOING COORDINATION	F

North Arrow

TRUE NORTH

This drawing has been prepared solely for the use of THE CHURCH OF JESUS CHRIST OF LATTER -DAY SAINTS and there are no representations of any kind made by NORR to any party with whom NORR has not entered into a contract.

This drawing shall not be used for construction purposes until the seal appearing hereon is signed and dated by the Architect or Engineer

Project Component
CONSTRUCTION DOCUMENTS

Key Plan

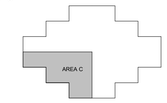

Consultants

Survey:	SIEGFRIED, 3428 BROOKSIDE ROAD, STOCKON, CA 95219
Civil:	SIEGFRIED, 3428 BROOKSIDE ROAD, STOCKON, CA 95219
Architectural:	NORR, 2020 I STREET, SUITE 200, SACRAMENTO, CA 95816
Structural:	BUEHLER, 600 Q STREET #200, SACRAMENTO, CA 95811
Mechanical:	GLUMAC, 150 S 4TH STREET UNIT A, HENDERSION, NV 89015
Electrical:	GLUMAC, 150 S 4TH STREET UNIT A, HENDERSION, NV 89015
Interiors:	SAGRADA, 965 N. DE SOTO ST E, SALT LAKE CITY, UT 84103
Landscape:	SIEGFRIED, 3428 BROOKSIDE ROAD, STOCKTON, CA 95219

Seal(s)

NORR
2020 I Street, Suite 200
Sacramento, CA 95816, United States
916.930.0210
norr.com

Project Manager: ANDREA JAGGERS	Drawn: Author
Project Leader: JULIAN ANDRADE	Checked: Checker

Client
THE CHURCH OF JESUS CHRIST OF LATTER-DAY SAINTS

Project
NEW TEMPLE PROJECT

771 W. Fremont Ave. Sunnyvale, CA 94087

Drawing Title
ENLARGED FLOOR PLAN - LEVEL 01 - AREA C

Scale: 1/4" = 1'-0"

Project No.: ED2024-0005-00

Drawing No.: **A20-07**

ARCH E Title Block - v.2024 - Rev (June/24) - Copyright © 2024

3/19/2025 11:37:49 AM
Autodesk Docs://LDS_Temple_San Jose, CA/NORR_ED2024-0005_JR_SanJoseTemple_Interior_R24.rvt